LRA Form No. PIA
30 March 1978

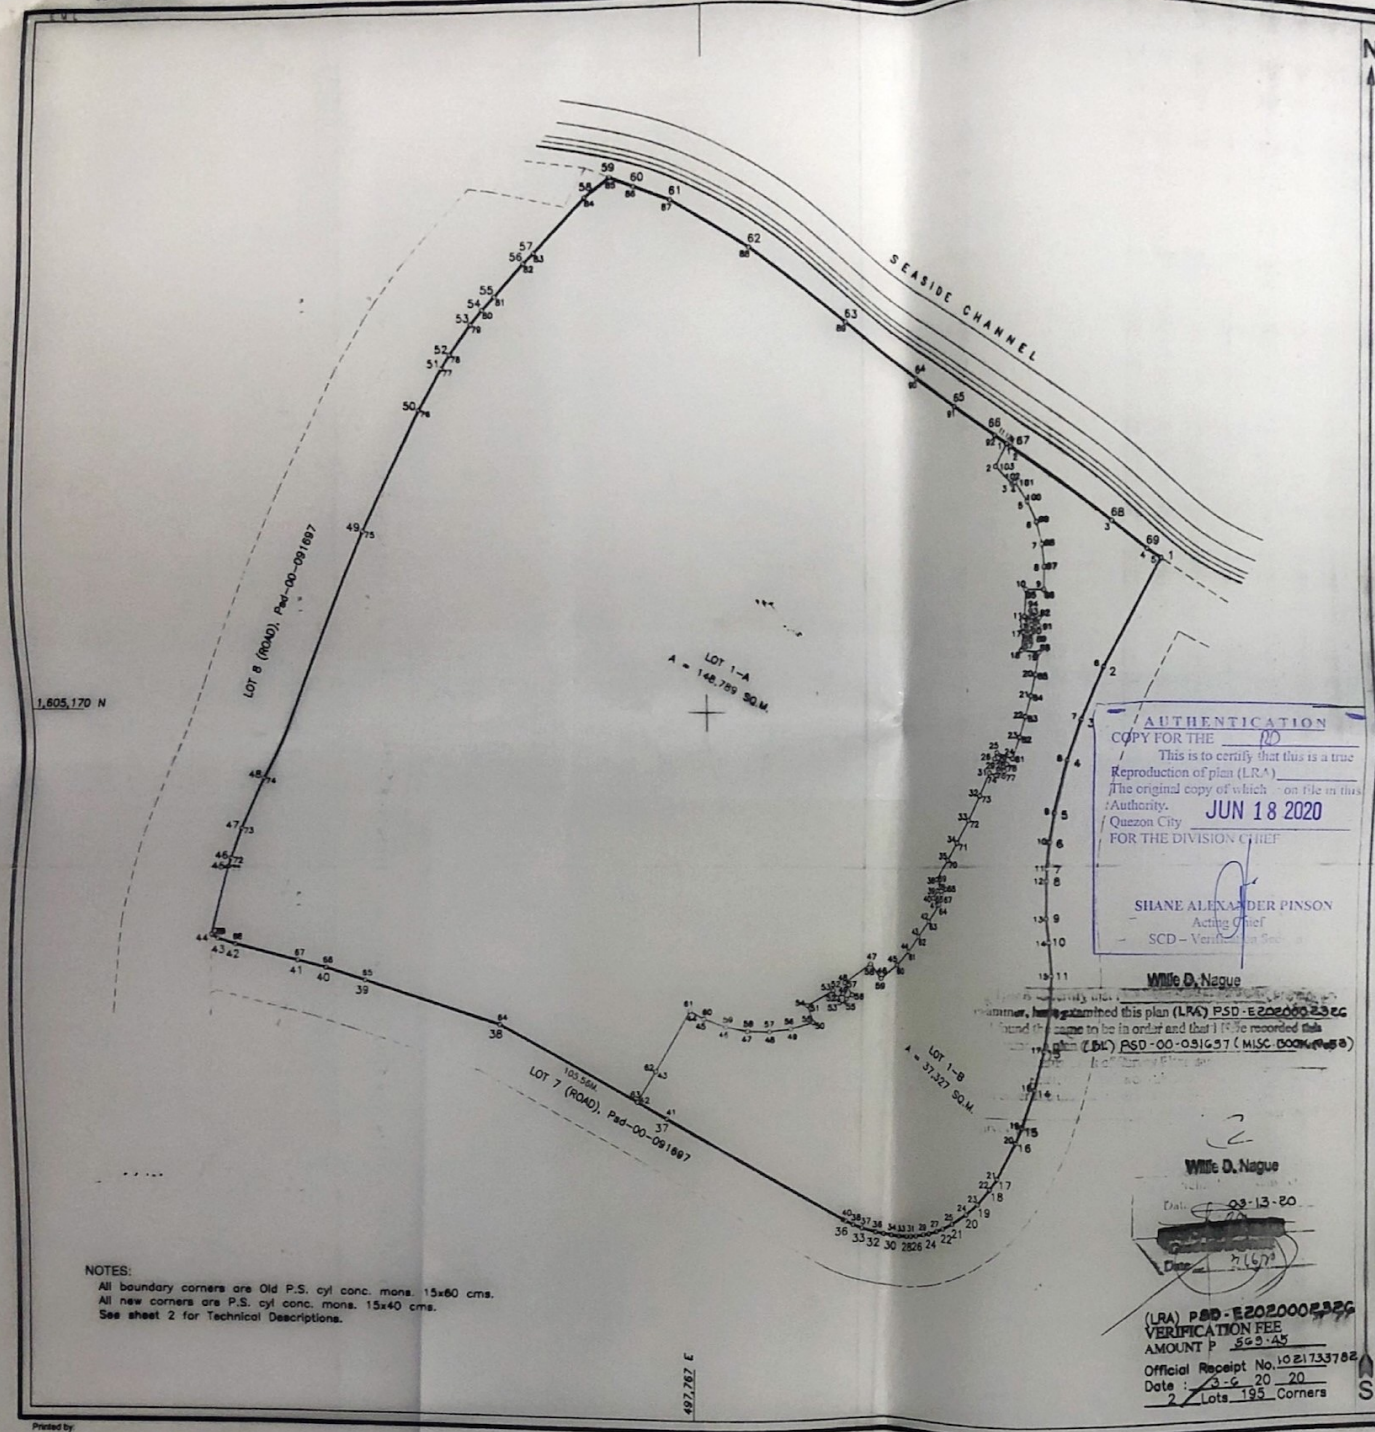

NOTES:
All boundary corners are Old P.S. cyl conc. mons. 15x60 cms.
All new corners are P.S. cyl conc. mons. 15x40 cms.
See sheet 2 for Technical Descriptions.

AUTHENTICATION
COPY FOR THE PD
This is to certify that this is a true Reproduction of plan (LRA) ____ The original copy of which is on file in this Authority.
Quezon City JUN 18 2020
FOR THE DIVISION CHIEF
SHANE ALEXANDER PINSON
Acting Chief
SCD – Verification Section

Willie D. Nague
Examiner, having examined this plan (LRA) PSD-E202000 2326 found the same to be in order and that it is recorded this plan (DL) PSD-00-091697 (MISC. BOOK 058)

Willie D. Nague
Date 03-13-20
Date 2/6/20

(LRA) PSD-E202000 2326
VERIFICATION FEE
AMOUNT P 569.45
Official Receipt No. 1021733782
Date : 3-6 20 20
2 Lots 195 Corners

LRA ..... REC. No. S. PATENT

PLAN

OF
SUBDIVISION SURVEY MADE FOR
EAGLE I LANDHOLDINGS, INC.
OF LOT 1, Psd-00-091697
DESCRIBED IN TCT No. 010-2016002791
ISSUED IN FAVOR OF
EAGLE I LANDHOLDINGS, INC.

SITUATED IN THE
RURBAN CODE : 04-03-16
BARRIO/DISTRICT OF: TAMBO
MUNI / CITY OF : PARAÑAQUE
PROVINCE OF : METRO MANILA
ISLAND OF : LUZON
CONTAINING AN AREA OF 186,116 SQ. M.
BEARINGS TRUE
SCALE 1 : 2000

0 10 20 50 100 200 m

I certify that this is a correct plan of the land survey herein plotted in accordance with the actual measurements and observations performed by me; that the boundaries of the property indicated to me by the owner or his authorized representative are identical with those stated in the Certificate of Title subject matter hereof; that the corners along the boundary of each lot shown in this plan are marked on the ground by concrete monuments or other visible marks as described; that there is no alteration of the boundary, perimeter aggregate area as appearing in the title(s) subject of the plan; that the survey and plat are both accurate; that the survey was executed with the full knowledge and consent of the owner(s); and that the survey was executed by me in conformity with the existing laws of the Republic of the Philippines and the regulations of the Land Registration Authority.

SURVEYED:
FEBUARY 8, 2016

CHERYL TOLOZA-MANALAYSAY
GEODETIC ENGINEER
Reg. Cert. No. 8197 Date: 10-26-2007
PTR No. 8021087 Date: 03-26-2019

ORIGINAL SURVEY: DECEMBER 1-7, 1976 (PARAÑAQUE CADASTRE)

Department of Justice
LAND REGISTRATION AUTHORITY

Verified and recommended for approval as SIMPLE plan.
Quezon City, ... 20

MARCO A. CASTRO
Acting Chief, Subdivision Division

PORFIRIO R. ELICEA, JR.
Director, Land Reg. Operations Service

Approved pursuant to P.D. 1529

Quezon City, Philippines JUNE 17 2020

BY AUTHORITY PURSUANT TO
A.O. NO. 2017-130, DTD. AUG. 8, 2017

0077873

ROBERT NOMAR V. LEYRETANA CERES
DEPUTY ADMINISTRATOR

Plotted on PIM/MIM No. ____ Date ____
Recorded by ____ Date ____
Plan checked against title ____ Date ____
Prel. Exam Willie D. Nague Date 03-13-20
Sec. Exam ____ Date ____
Final Exam ____ Date 2/6/20
Additional information and remarks ____

SUBJECT TO WHATEVER SUBSISTING ENCUMBRANCES AND TO THE CONDITION IMPOSE ON PATENT TITLE.

Sheet 1 of 2 sheets

(LRA) Psd - E202000 2326

Printed by
POLAR MATRIX ENGINEERING SERVICES
Unit 210, PMHA Bldg. No. 18 V. Luna corner East Ave.,
Pinyahan, Quezon City / Tel. (02) 7756-15-26, Email: polar matrix@yahoo.com
Authorized by The Land Management Bureau
Until June 24, 2002

LRA Form No. PIA
30 March 1976

TECHNICAL DESCRIPTION

LINES	BEARINGS	DISTANCES
CONSOLIDATION BOUNDARY		
1-2	N 61° 10' W	29.88M
2-3	N 61° 10' W	84.34M
3-4	N 61° 10' W	25.88M
4-5	N 61° 10' W	62.34M
5-6	N 61° 10' W	22.35M
6-7	N 16° 10' W	4.00M
7-8	S 28° 50' W	25.88M
8-9	S 28° 50' W	47.17M
9-10	S 28° 50' W	47.17M
10-11	S 28° 50' W	40.16M
11-12	S 28° 50' W	47.17M
12-13	S 28° 50' W	47.17M
13-14	S 28° 50' W	25.88M
14-15	S 28° 50' W	247.87M
15-16	N 58° 23' W	28.53M
16-17	N 28° 50' E	29.87M
17-18	N 28° 50' E	33.72M
18-19	N 28° 50' E	33.65M
19-20	N 28° 50' E	33.67M
20-21	N 28° 50' E	33.98M
21-22	N 28° 50' E	34.02M
22-23	N 28° 50' E	34.11M
23-24	N 28° 50' E	34.17M
24-25	N 28° 50' E	34.27M
25-26	N 28° 50' E	16.79M
26-27	N 28° 50' E	16.55M
27-28	N 28° 50' E	34.41M
28-29	N 28° 50' E	34.50M
29-30	N 28° 50' E	34.58M
30-31	N 28° 50' E	34.68M
31-32	N 28° 50' E	34.73M
32-33	N 61° 10' W	86.26M
33-34	N 29° 10' E	34.02M
34-35	N 29° 10' E	34.90M
35-36	N 29° 10' E	34.98M
36-37	N 29° 10' E	35.05M
37-38	N 29° 10' E	35.15M
38-39	N 29° 10' E	35.24M
39-40	N 29° 10' E	7.61M
40-41	N 25° 59' E	19.62M
41-42	N 23° 56' E	237.00M
42-43	S 62° 39' E	71.38M
43-44	S 78° 03' E	42.12M
44-45	N 25° 39' E	3.84M
45-46	N 25° 39' E	20.17M
46-47	S 68° 47' E	26.33M
47-48	S 68° 47' E	21.60M
48-49	S 59° 34' E	49.03M
49-50	S 54° 56' E	64.84M
50-51	S 54° 56' E	55.22M
51-52	S 54° 56' E	34.63M
52-53	S 54° 56' E	31.35M
53-54	S 54° 56' E	11.12M
54-55	S 54° 56' E	68.00M
55-56	S 54° 56' E	24.21M
56-57	S 58° 18' E	40.77M
57-58	S 58° 18' E	9.40M
58-59	S 61° 01' E	50.22M
59-60	S 70° 46' E	10.12M
60-61	S 76° 46' E	40.10M
61-62	S 81° 07' E	27.75M
62-63	S 81° 07' E	15.22M
63-64	S 81° 07' E	50.00M
64-65	S 88° 50' E	13.61M
65-66	S 88° 50' E	52.38M
66-67	S 28° 26' W	10.28M
67-68	S 28° 26' W	11.38M
68-69	S 28° 26' W	15.64M
69-70	N 11° 26' W	3.63M
70-71	N 80° 53' W	132.50M
71-72	N 78° 25' W	30.00M
72-73	N 77° 33' W	30.01M
73-74	N 68° 40' W	29.99M
74-75	N 62° 58' W	28.48M
75-76	S 27° 04' W	44.39M
76-77	S 20° 28' W	29.08M
77-78	S 20° 28' W	18.60M
78-79	S 07° 34' W	37.88M
79-80	S 02° 56' E	29.34M
80-81	S 17° 12' E	10.31M
81-82	S 61° 25' E	36.71M
82-83	S 73° 57' E	75.06M
83-84	S 62° 56' E	72.44M
84-85	S 28° 27' W	60.13M
85-86	S 72° 42' W	4.00M

CONSOLIDATION BOUNDARY (CONT.)		
86-87	S 28° 27' W	23.13M
87-88	S 28° 27' W	256.60M
88-89	S 28° 27' W	25.60M
89-90	S 28° 27' W	52.19M
90-91	S 72° 23' W	4.60M
91-92	N 61° 33' W	89.46M
92-93	N 61° 33' W	91.70M
93-94	N 61° 33' W	69.44M
94-95	N 61° 33' W	68.35M
95-96	N 16° 10' W	4.00M
96-97	N 28° 50' E	84.23M
97-98	N 28° 50' E	22.83M
98-99	N 61° 10' W	27.83M
99-1	N 61° 10' W	84.34M
LOT 1-A		
1-2	S 28° 36' W	13.18M
2-3	S 44° 29' E	13.97M
3-4	N 53° 22' E	1.78M
4-5	S 34° 02' E	12.44M
5-6	S 24° 55' E	12.17M
6-7	S 16° 19' E	12.14M
7-8	S 07° 03' E	12.04M
8-9	S 00° 05' W	11.98M
9-10	N 89° 01' W	9.87M
10-11	S 02° 55' W	14.22M
11-12	S 83° 28' E	4.45M
12-13	S 83° 28' E	3.63M
13-14	S 05° 06' W	4.07M
14-15	N 83° 28' W	3.73M
15-16	S 06° 32' W	4.18M
16-17	N 83° 30' W	4.02M
17-18	S 06° 30' W	5.66M
18-19	S 81° 31' E	3.72M
19-20	S 06° 40' W	11.84M
20-21	S 11° 55' W	11.45M
21-22	S 14° 20' W	11.37M
22-23	S 16° 15' W	11.44M
23-24	S 10° 41' W	11.91M
24-25	N 70° 12' W	5.69M
25-26	S 21° 32' W	3.48M
26-27	S 67° 42' E	7.77M
27-28	S 20° 50' W	4.07M
28-29	N 67° 42' W	3.74M
29-30	S 22° 18' W	3.97M
30-31	N 66° 29' W	4.10M
31-32	S 24° 27' W	13.50M
32-33	S 27° 35' W	14.65M
33-34	S 39° 39' W	14.09M
34-35	S 53° 31' W	11.03M
35-36	S 37° 16' W	12.90M
36-37	S 49° 35' E	6.16M
37-38	S 42° 01' W	4.05M
38-39	N 49° 35' W	3.58M
39-40	S 49° 25' W	5.29M
40-41	S 50° 24' E	3.75M
41-42	S 41° 03' W	11.91M
42-43	S 43° 40' W	11.43M
43-44	S 45° 56' W	11.37M
44-45	S 48° 15' W	11.53M
45-46	S 50° 24' W	11.77M
46-47	N 38° 20' W	9.91M
47-48	S 54° 20' W	17.03M
48-49	S 33° 16' E	7.90M
49-50	S 58° 11' W	4.07M
50-51	N 33° 16' W	3.91M
51-52	S 58° 44' W	4.17M
52-53	N 29° 14' W	4.56M
53-54	S 60° 46' W	16.75M
54-55	S 20° 58' E	9.76M
55-56	S 73° 47' W	13.02M
56-57	S 62° 01' W	11.73M
57-58	N 88° 58' W	12.01M
58-59	N 78° 25' W	12.12M
59-60	N 88° 50' W	12.71M
60-61	N 61° 03' W	8.62M
61-62	S 28° 55' W	37.05M
62-63	S 31° 16' W	33.36M
63-64	N 61° 28' W	86.93M
64-65	N 71° 42' W	76.66M
65-66	N 72° 17' W	32.20M
66-67	N 78° 04' W	13.76M
67-68	N 73° 40' W	35.10M
68-69	N 73° 01' W	10.23M
69-70	N 58° 06' W	4.00M
70-71	N 12° 08' E	37.47M
71-72	N 15° 37' E	4.04M
72-73	N 15° 37' E	17.33M

LOT 1-A (CONT.)		
73-74	N 20° 00' E	30.21M
74-75	N 23° 23' E	145.40M
75-76	N 24° 23' E	72.37M
76-77	N 28° 46' E	25.61M
77-78	N 32° 39' E	8.69M
78-79	N 36° 24' E	19.67M
79-80	N 40° 29' E	9.54M
80-81	N 43° 48' E	9.69M
81-82	N 41° 50' E	23.95M
82-83	N 45° 41' E	7.96M
83-84	N 42° 46' E	40.55M
84-85	N 51° 19' E	17.44M
85-86	S 68° 47' E	14.39M
86-87	S 68° 47' E	21.60M
87-88	S 59° 34' E	49.03M
88-89	S 54° 56' E	64.84M
89-90	S 54° 56' E	55.22M
90-91	S 54° 56' E	34.63M
91-92	S 54° 56' E	31.35M
92-1	S 54° 56' E	6.64M
LOT 1-B		
1-2	S 54° 56' E	2.48M
2-3	S 54° 56' E	66.56M
3-4	S 54° 56' E	24.21M
4-5	S 66° 18' E	9.01M
5-6	S 27° 30' W	66.34M
6-7	S 23° 09' W	30.92M
7-8	S 18° 39' W	22.64M
8-9	S 13° 41' W	22.76M
9-10	S 09° 39' W	15.87M
10-11	S 05° 29' W	14.44M
11-12	S 02° 35' W	6.28M
12-13	S 00° 23' W	19.99M
13-14	S 06° 23' E	12.81M
14-15	S 04° 00' E	17.81M
15-16	S 02° 43' W	20.31M
16-17	S 05° 59' W	20.28M
17-18	S 14° 06' W	21.01M
18-19	S 15° 02' W	21.20M
19-20	S 23° 29' W	8.76M
20-21	S 28° 08' W	21.60M
21-22	S 36° 50' W	7.01M
22-23	S 40° 14' W	10.83M
23-24	S 50° 25' W	8.77M
24-25	S 57° 12' W	10.48M
25-26	S 63° 56' W	6.73M
26-27	S 66° 18' W	4.86M
27-28	S 72° 15' W	5.67M
28-29	S 76° 50' W	4.08M
29-30	S 79° 43' W	5.43M
30-31	S 83° 58' W	3.86M
31-32	S 86° 41' W	5.08M
32-33	S 89° 12' W	5.51M
33-34	N 85° 55' W	4.71M
34-35	N 82° 47' W	4.87M
35-36	N 78° 37' W	4.79M
36-37	N 74° 32' W	7.88M
37-38	N 69° 06' W	5.39M
38-39	N 64° 22' W	4.73M
39-40	N 61° 42' W	1.66M
40-41	N 61° 20' W	112.77M
41-42	N 61° 35' W	18.71M
42-43	N 31° 16' E	19.38M
43-44	N 22° 55' E	37.05M
44-45	N 61° 35' E	8.62M
45-46	S 88° 50' E	12.71M
46-47	S 76° 20' E	12.12M
47-48	S 68° 58' E	12.01M
48-49	N 82° 21' E	11.73M
49-50	N 73° 47' E	13.02M
50-51	N 20° 58' W	9.76M
51-52	N 60° 46' E	16.75M
52-53	S 29° 14' E	4.56M
53-54	N 58° 44' E	4.17M
54-55	S 31° 16' E	3.63M
55-56	N 88° 11' E	4.07M
56-57	N 33° 16' W	7.00M
57-58	N 54° 39' E	17.93M
58-59	S 38° 20' E	6.31M
59-60	N 80° 24' E	11.77M
60-61	N 48° 18' E	11.53M
61-62	N 45° 59' E	11.37M
62-63	N 43° 40' E	11.43M
63-64	N 41° 03' E	11.91M
64-65	N 50° 24' W	5.79M
65-66	N 40° 20' E	5.29M
66-67	N 49° 35' E	3.58M
67-68	N 42° 01' E	4.05M

68-69	N 49° 35' W	3.16M
69-70	N 37° 15' E	12.90M
70-71	N 31° 31' E	11.23M
71-72	N 30° 39' E	14.09M
72-73	N 27° 35' E	14.66M
73-74	N 24° 27' E	12.55M
74-75	S 64° 29' E	4.10M
75-76	N 21° 18' E	3.97M
76-77	S 61° 42' E	3.74M
77-78	N 20° 50' E	4.07M
78-79	N 61° 42' W	7.77M
79-80	N 2° 13' E	3.48M
80-81	S 70° 2' E	3.68M
81-82	N 18° 41' E	11.91M
82-83	N 16° 15' E	11.44M
83-84	N 14° 28' E	11.37M
84-85	N 11° 58' E	11.49M
85-86	N 64° 46' E	11.94M
86-87	N 61° 11' W	9.72M
87-88	N 90° 38' E	9.66M
88-89	S 81° 35' E	4.52M
89-90	N 90° 32' E	4.18M
90-91	S 82° 29' E	3.73M
91-92	N 85° 06' E	4.07M
92-93	N 82° 28' W	3.63M
93-94	N 82° 28' W	4.45M
94-95	N 02° 55' E	14.22M
95-96	S 89° 01' E	3.67M
96-97	N 00° 05' E	11.98M
97-98	N 07° 05' W	12.04M
98-99	N 16° 19' W	12.14M
99-100	N 24° 55' W	12.17M
100-101	N 34° 02' W	12.44M
101-102	S 62° 22' W	1.78M
102-103	N 44° 29' W	13.97M
103-1	N 28° 36' E	13.18M

Tie lines from BLLM # 11
PASAY (BWD-41756) to Corner
Marked "1"

LOT NO.	BEARINGS	DISTANCES
C.BDRY	S 15° 47' W	3,441.12M
LOT 1-A	S 17° 26' W	3,442.62M
LOT 1-B	S 17° 26' W	3,412.62M

NOTES:
All boundary corners are Old P.S. cyl conc. mons. 15x60 cms.
All new corners are P.S. cyl conc. mons. 15x40 cms.

Willie D. Nagui
[illegible] examined this plan (LRA) PSD-[illegible]
[illegible] the same to be in order and that it is to be mounted [illegible]
(SLT 09-00-091697 [illegible])

ALTERNATIVE COPY FOR USE
This is to certify that this is a true Reproduction of the Original (LRA) The original copy of which [illegible] Authority.
Quezon City, JUN 18 2020
FOR THE [illegible]
SHANE ALEXANDER PINSON
Acting [illegible]
SCD - Verification [illegible]

Willie D. Nagui
[illegible]
Date 03-18-20
[illegible]

(LRA) PSD-E202000 2326
VERIFICATION FEE
AMOUNT P 265.45
Official Receipt No. 09217[illegible]
Date 3-16 20 20
2 Lots 195 Corners

N LRA REC. No. 5 PATENT

PLAN

TECHNICAL DESCRIPTION OF
SUBDIVISION SURVEY MADE FOR
EAGLE I LANDHOLDINGS, INC.

OF **LOT 1, Psd-00-091697**

DESCRIBED IN TCT No. 010-2016002791
ISSUED IN FAVOR OF

EAGLE I LANDHOLDINGS, INC.

SITUATED IN THE
BURIAN CODE : 64-03-16
BARIO/BARRIO OF: TAMBO
MUNI. / CITY OF : PARAÑAQUE
PROVINCE OF : METRO MANILA
ISLAND OF : LUZON

CONTAINING AN AREA OF **SEE SHEET 1** SQ. M.

BEARINGS TRUE
SCALE 1 : 2000

I certify that this is a correct plan of the land survey herein plotted in accordance with the actual measurements and observations performed by me; that the boundaries of the property indicated to me by the owner or his authorized representative are identical with those stated in the Certificate of Title subject matter hereof; that the corners along the boundary of each lot shown in this plan are marked on the ground by concrete monuments or other visible marks as described; that there is no alteration of the boundary, perimeter aggregate area as appearing in the title(s) subject of the plan; that the survey and plat are both accurate; that the survey was executed with the full knowledge and consent of the owner(s); and that the survey was executed by me in conformity with the existing laws of the Republic of the Philippines and the regulations of the Land Registration Authority.

SURVEYED:

CHERYL TORIZA-MANALAYSAY
GEODETIC ENGINEER
Reg. Cert. No. 8197 Date 10-28-2007
PTR No. 8021087 Date 03-28-2019

ORIGINAL SURVEY: DECEMBER 1-7, 1976 (PARAÑAQUE CADASTRE)

Department of Justice
LAND REGISTRATION AUTHORITY

Verified and recommended for approval as SIMPLE plan.
Quezon City, 20

MARCO A. CASTRO
Acting

FORWARD [illegible]
Geodetic Engineer, Land Reg. Operations Services

Approved pursuant to P.D. 1529
Quezon City, Philippines JUNE 17 20 20

BY AUTHORITY PURSUANT TO
A.O. No. 2017-026, DTD. AUG. 8, 2017

ROBERT [illegible] V. LIVERETAMA CESO II
Acting Administrator

0077873

Filed on PIS/MM No. _____ Date _____
Recorded by _____ Date _____
Plan checked _____ Date _____
Prel. Exam _____ Date 03-18-20
Sec. Exam _____ Date _____
Final Exam _____ Date JUN 17
Additional information and remarks _____
SUBJECT TO VARIOUS SUBSISTING ENCUMBRANCES AND TO THE CONDITIONS IMPOSED ON PATENT TITLE

Sheet 1 of 2 sheets

(LRA) Psd - E202000 2326

Prepared by
POLAR METRIC ENGINEERING SERVICES
Unit 210, Palace Bldg. No. 18 V. Luna corner Kalayaan
Pinyahan, Quezon City Tel. (02) 7789-15-28, Email: polar metric@yahoo.com
Authorized by The Land Management Bureau
Until June 24, 2021